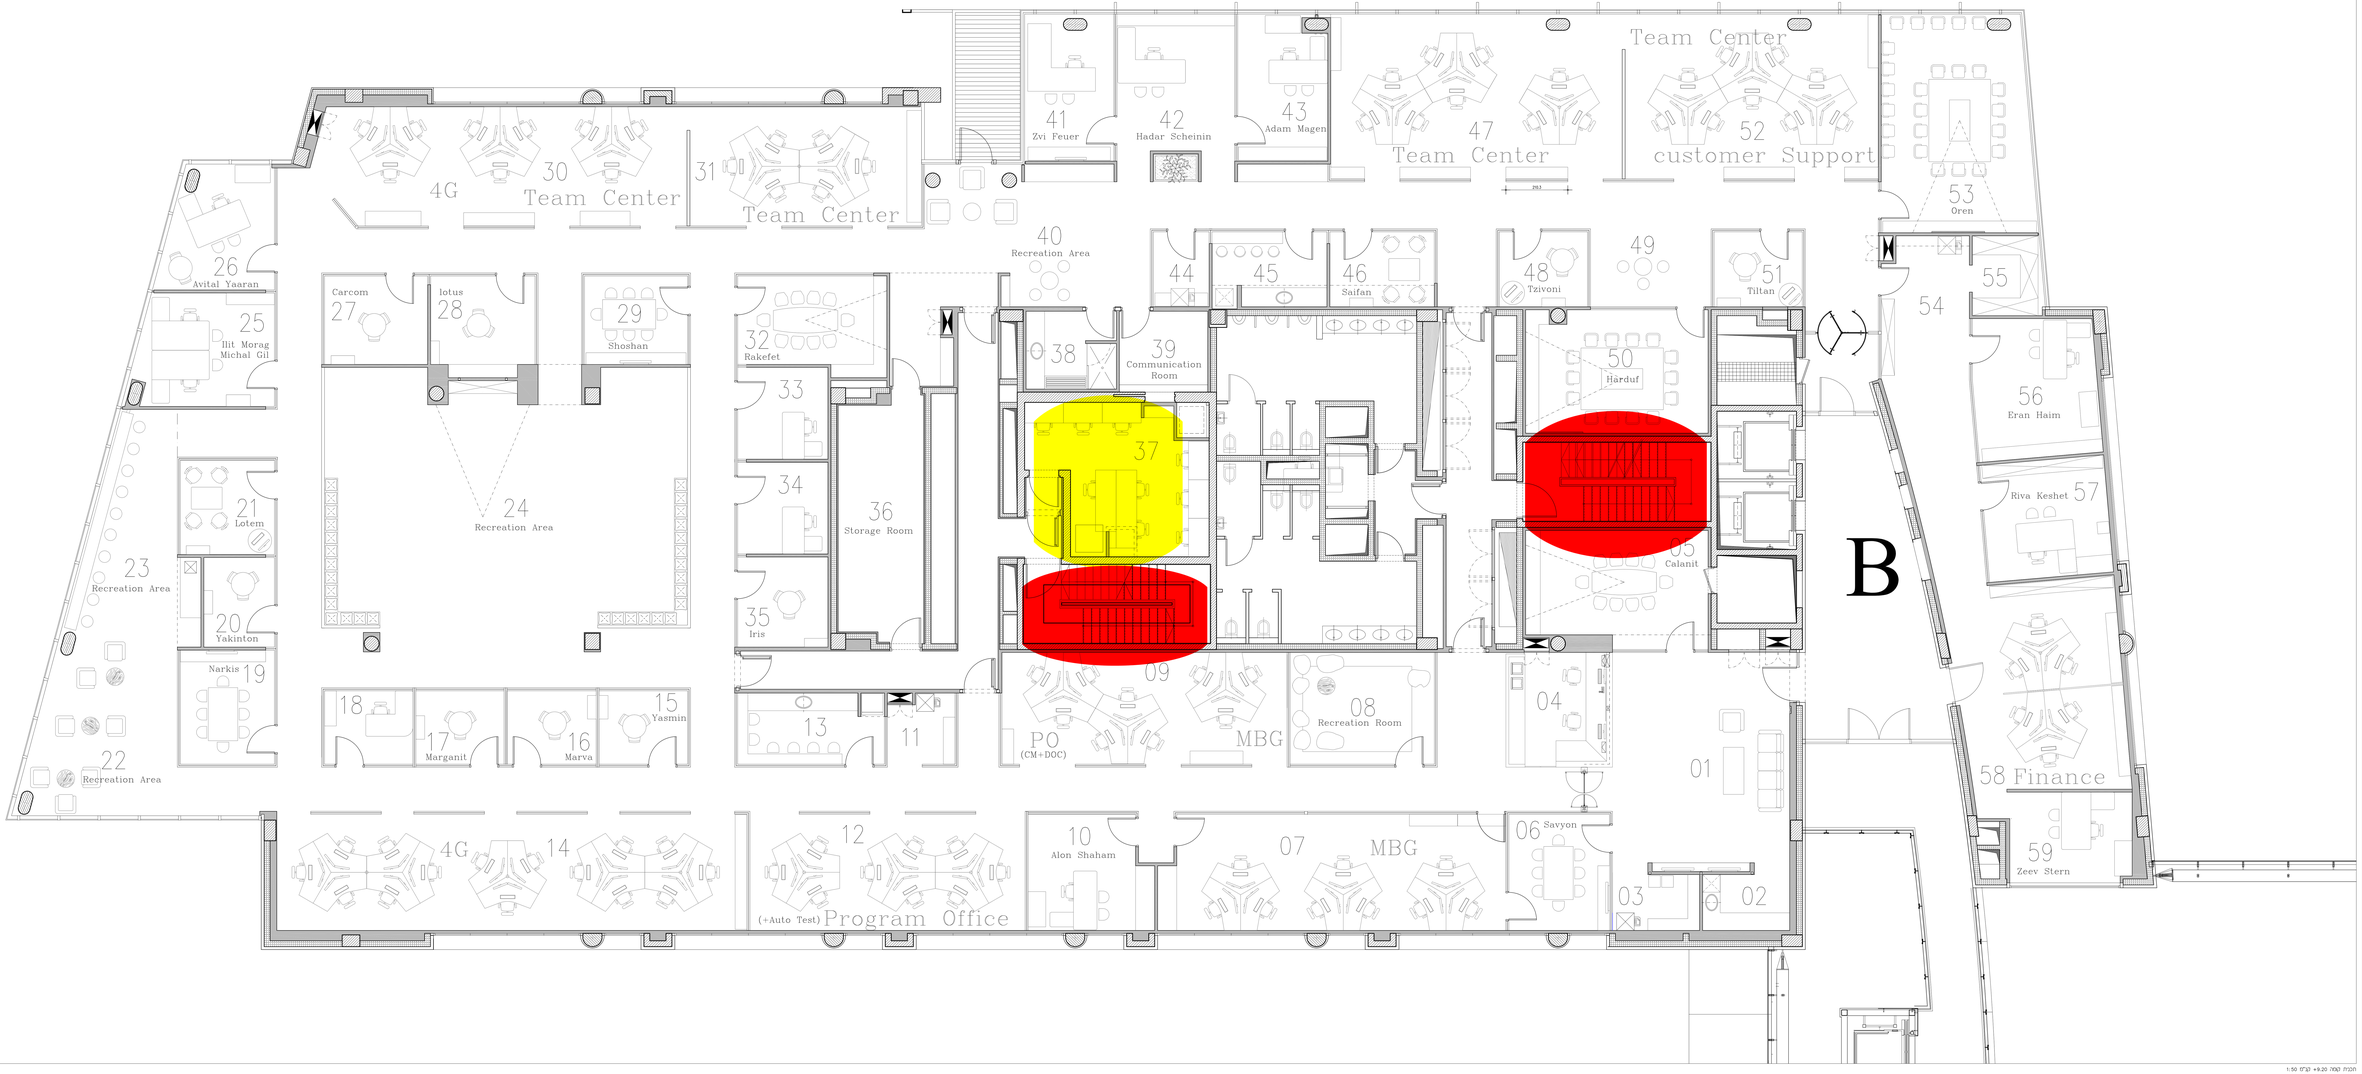


מהדורה	תיאור	תאריך
4	פיקוח	16.07.12
	יועצים	19.07.12
	יועצי פיקוח	25.07.12
	יועצי פיקוח	30.07.12
	קבלן מסגרי	30.08.12
	קבלן מכונאי	02.10.12
	קבלן מכונאי	08.11.12

סוג השרטוט	סדרה
תכנית לביצוע	A, B, C
ציוות כיתות לביצוע	A, B, C
ציוות כיתות לביצוע	A, B, C
ציוות כיתות לביצוע	A, B, C

מהדורה: 4 — 08-11-12

עדכון: 08.11.2012

לעיון / לאישור / למסגרן / לביצוע

שם גליון: A00 — תכנית קומה 9.20+

סביבה סטרואלה – סטמנס חוכנה בנין 8

מספר פרוייקט:	ARPT-2011
קנ"מ:	1:50
מפלס:	+9.20
קומה:	02
שם הקובץ:	ARPT-pl+9.20

SKORKA XMLINO ARCHITECTS
סקורקא חמלינו אדריכלים
Gil Yam 46905
09-9578000 טל'
09-9568570 פקס'
office@skorka-arch.com

תכנית קומה 9.20+ קנ"מ 1:50