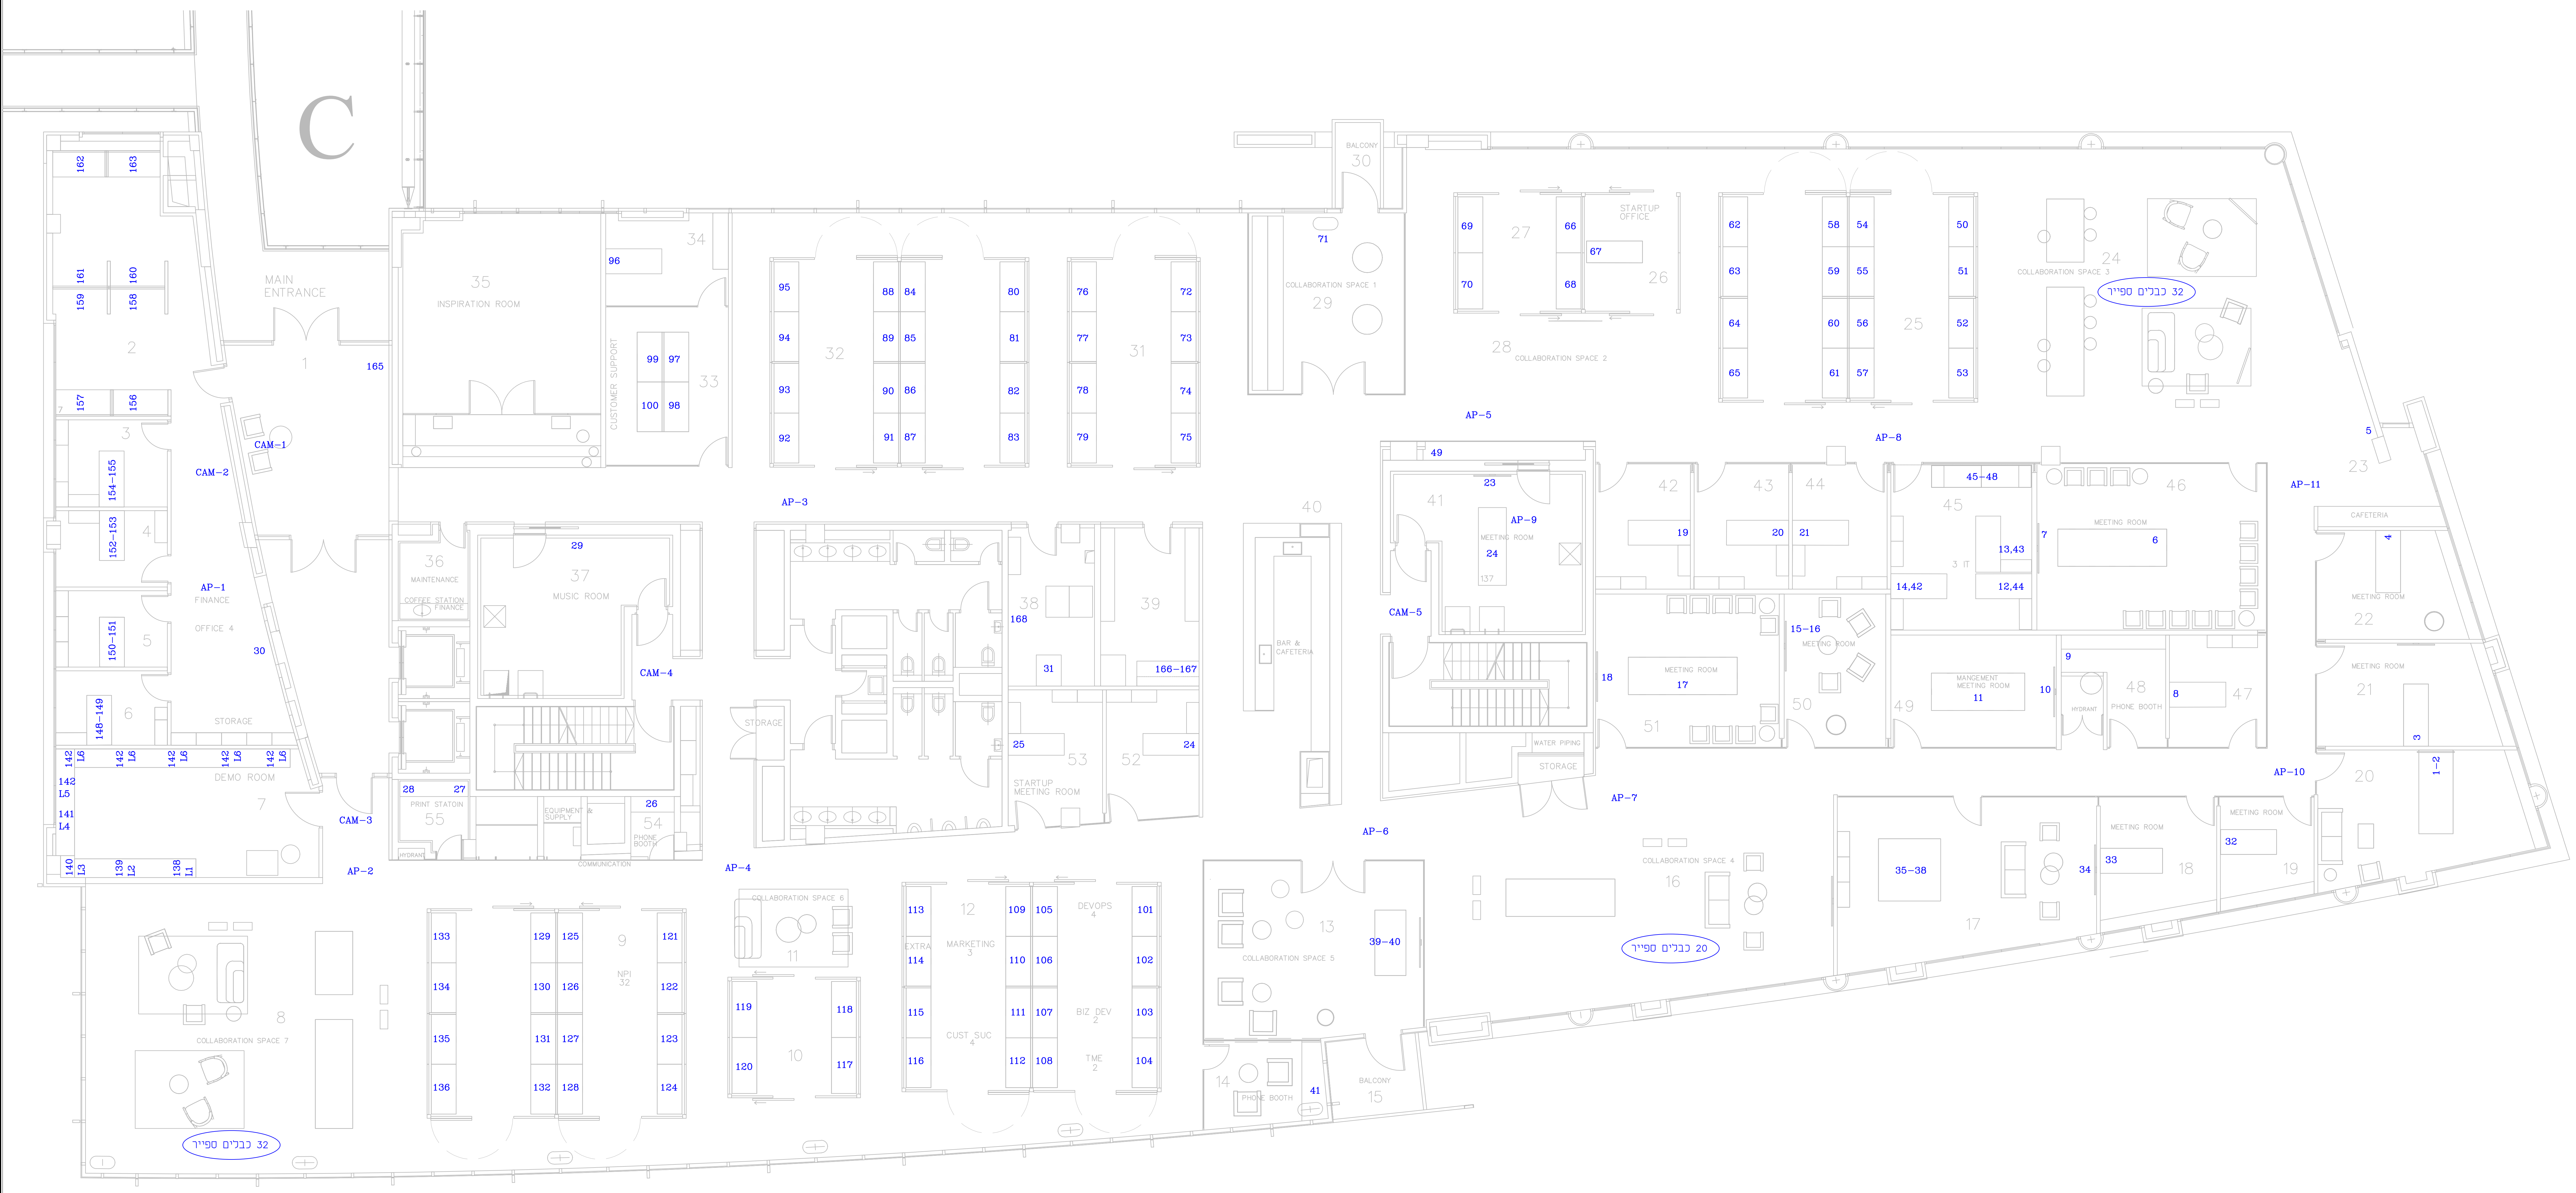

REV: מהדורה	DATE: תאריך	DESCRIPTION: מהות השינוי	DRAWN: שרטט	CHECKED: אישר

KEYPLAN: תכנית מפתח:

בינת יישום מערכות

Bynet System Applications

רח' ראול ולנברג 24
תל אביב 69719
TEL. 972-77-2715331 טלפון
FAX 972-3-6499640 פקס
24 RAUL WALENBERG ST.
TEL AVIV 69719
WWW.BYNET-YESUM.CO.IL

PROJECT NAME: שם הפרוייקט:

סימנס

DRAWING TITLE: נושא השרטוט:

איירפורט סיטי
קומה 3
פריסת נקודות תקשורת

FILE NAME : שם הקובץ:

70772-K3-01

PROJECT NO. : מס' פרוייקט:	SHEET : גיליון:	REV : מהדורה:
70772		0A

LAST UPDATE : 23.12.20 : תאריך שינוי אחרון

DATE: תאריך:	NAME: שם:		SCALE: קנה מידה:
	PREPARED BY: הכין:	יגאל אוחיון	
23.12.20	DRAWN: שרטט:	ניר	PAPER: גודל נייר: A1
	CONFIRMED: אישר:	יגאל אוחיון	

18-2 : סיווג